


Rev	Date	Iss. By	App. By	Description
P01	22/10/25	AZ	BM	First Issue
P02	31/10/25	BM	BM	Additional notes and surfaces added
P03	21/11/25	AZ	BM	Road Surface amendment, Boundary treatment legend amended as per comments received.

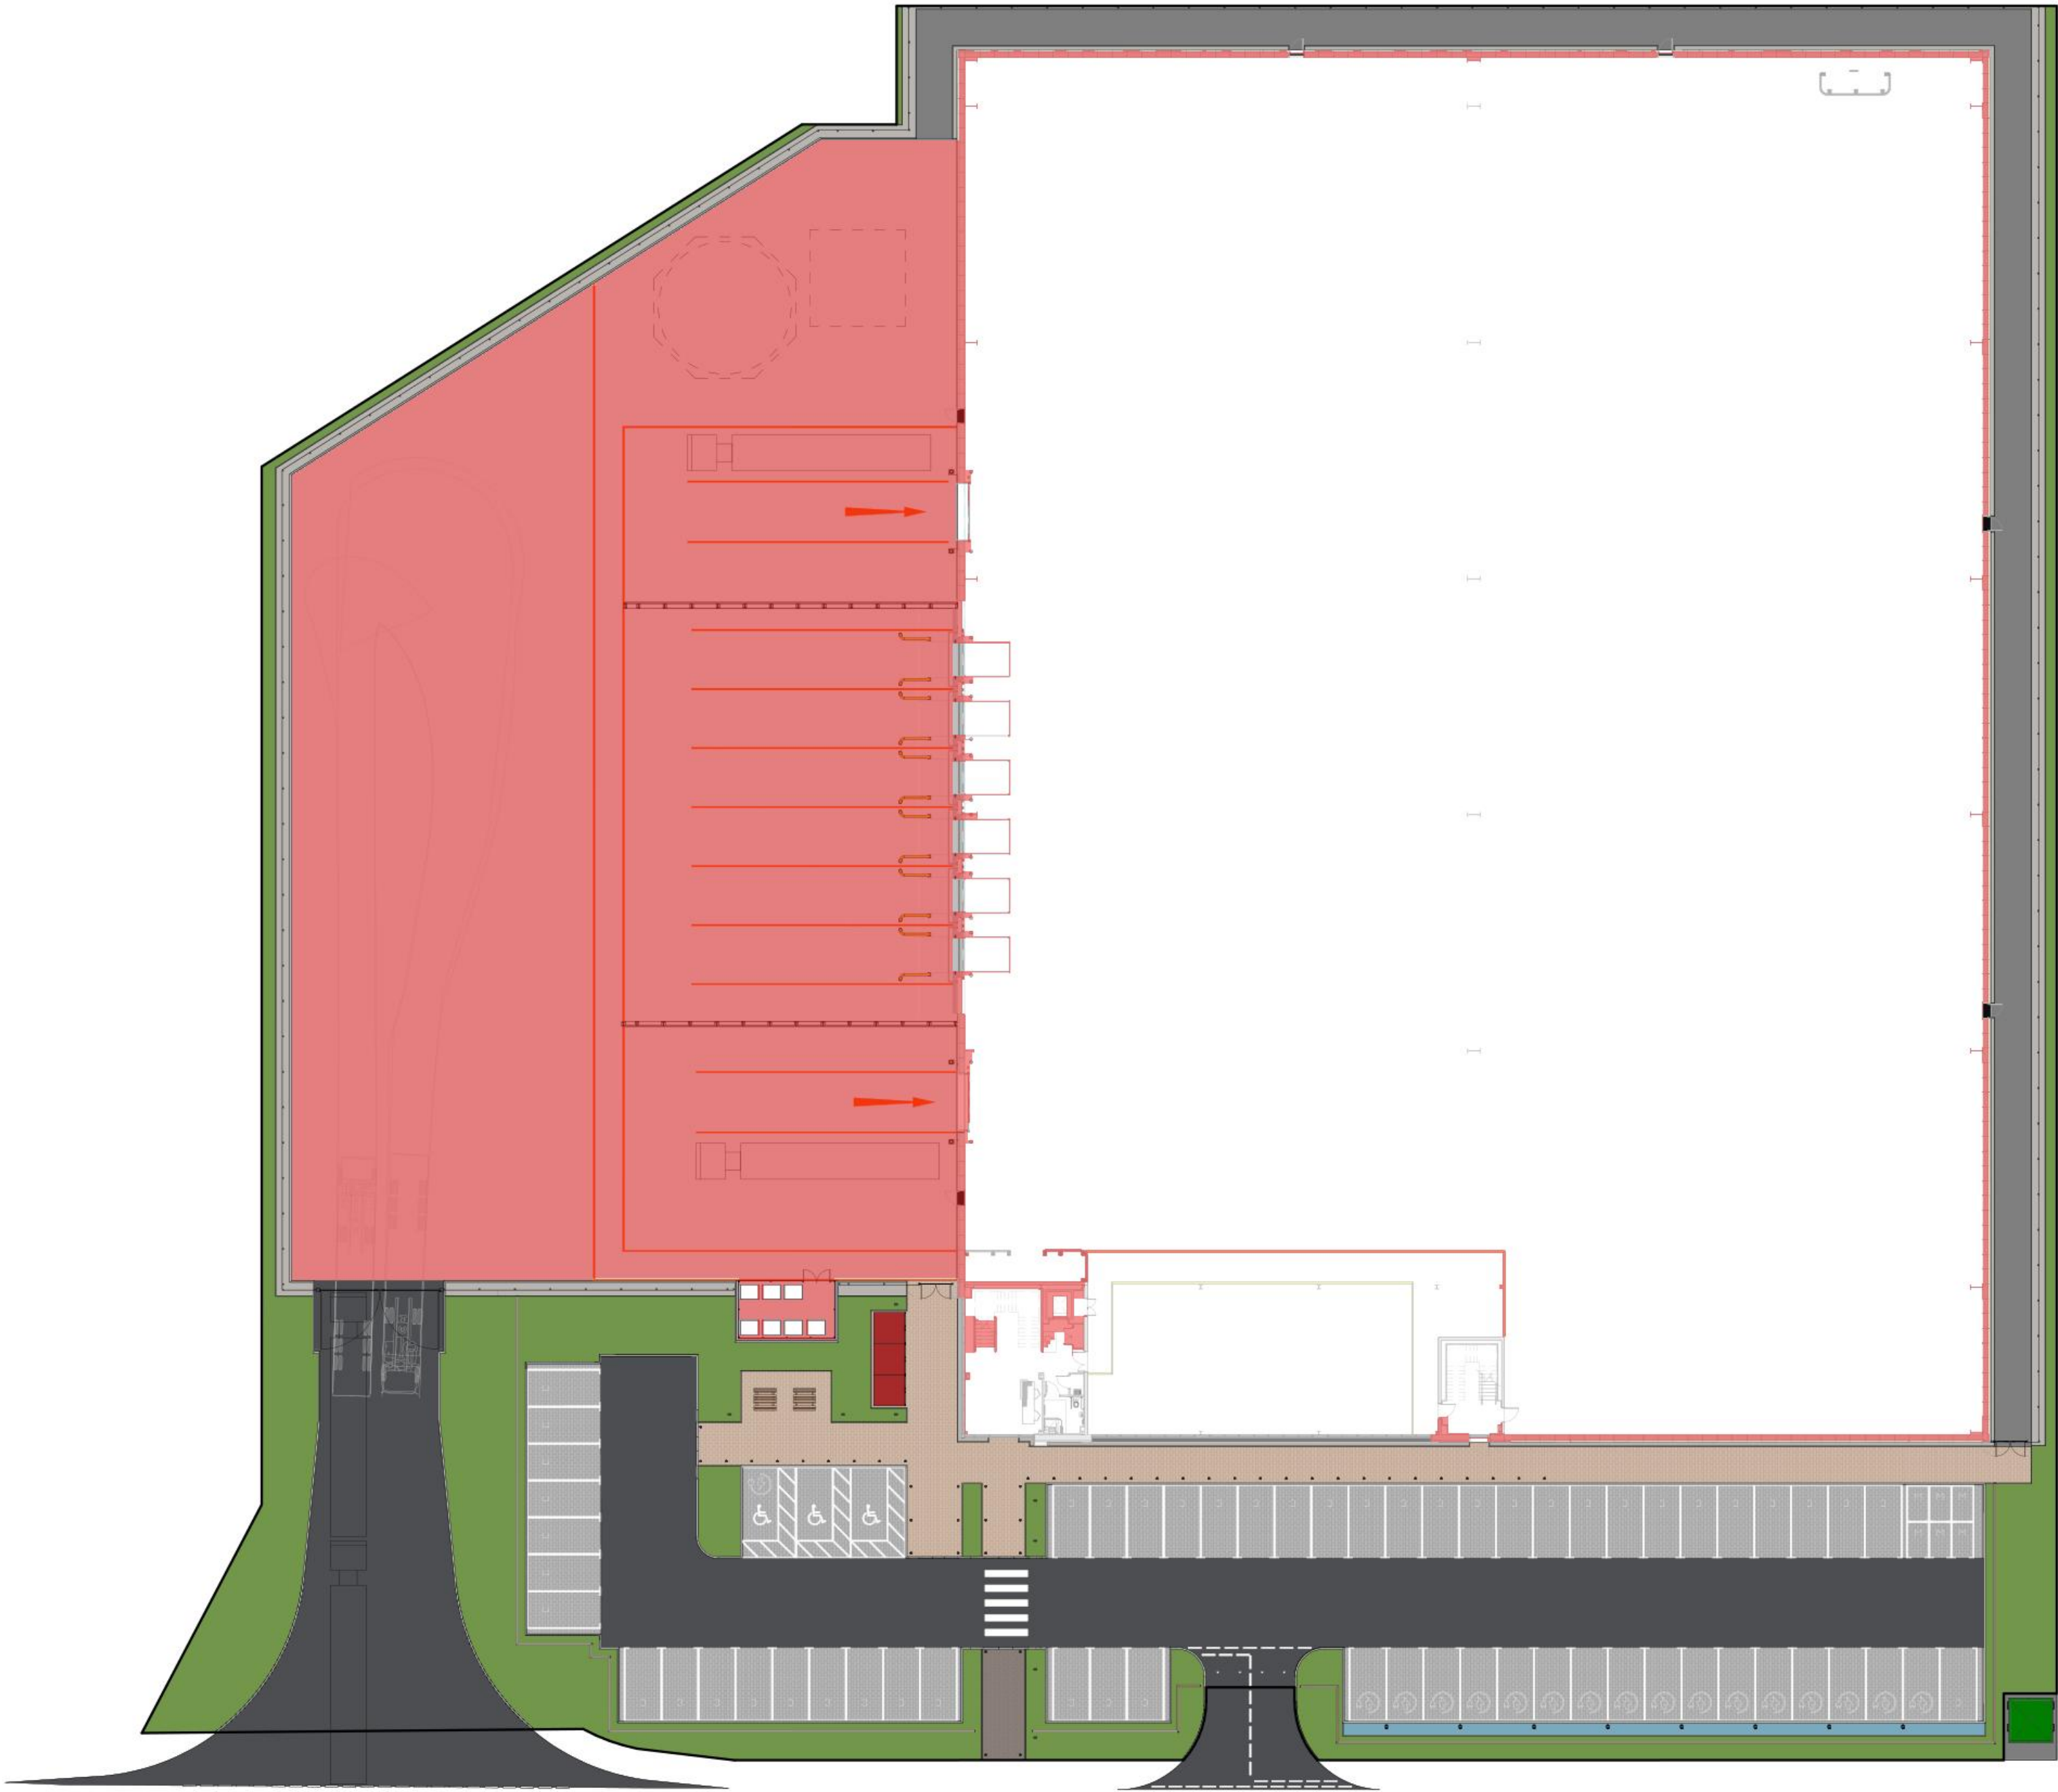

HARD LANDSCAPING LEGEND

Boundaries

 Plot Site Boundary

External Hard Surfacing

 Concrete Service Yard construction

 Roads:
Bituminous macadam with concrete edgings & kerbs

 Car Park Spaces:
Tobermore Fusion / Hydropave Fusion (red hatch)
200 x 100 x 80mm (Silver / Stretcher Bond) Space
demarcation with graphite blocks

 Footpaths (Feature):
Tobermore Fusion (Stretcher Bond)
200 x 100 x 60mm / Silver & Graphite

 Footpaths (Secondary): Tobermore Fusion
200 x 100 x 60mm / Silver

 EV charger zone:
Tobermore Fusion (stretcher bond)
200 x 100 x 60mm (Graphite)

 Footpaths (Ancillary): Concrete

 Gravel margin

 Soft Landscaping:
To Landscape Architect's details

 Grasscrete

 Water:
To Landscape Architect's details



SGP

Architects + Masterplanners

Waterfront House
2a Smith Way
Grove Park
Enderby
Leicester LE19 1SX

t: +44 (0)116 247 0557

www.stephengeorge.co.uk

Hemington, Castle Donington

Drawing Name:
Unit 1 (D77) - Hard Landscaping

Drawing Stage: **PLANNING**

Status: **S2**

SGP File Ref: 16-115-SGP-ZZ-ZZ-M3 A-131001 Unit 1

16-115-02	22/10/25	AZ	LVA	As indicated @A1	P03
SGP Project No	Date	Drawn	Team	Scale	Rev

Drawing Number: 105301-SGP-01-ZZ-DR-A-131002



SCALE 1:250
5m 25m

Unit 1 (D77) - Hard Landscaping Plan

1 : 250